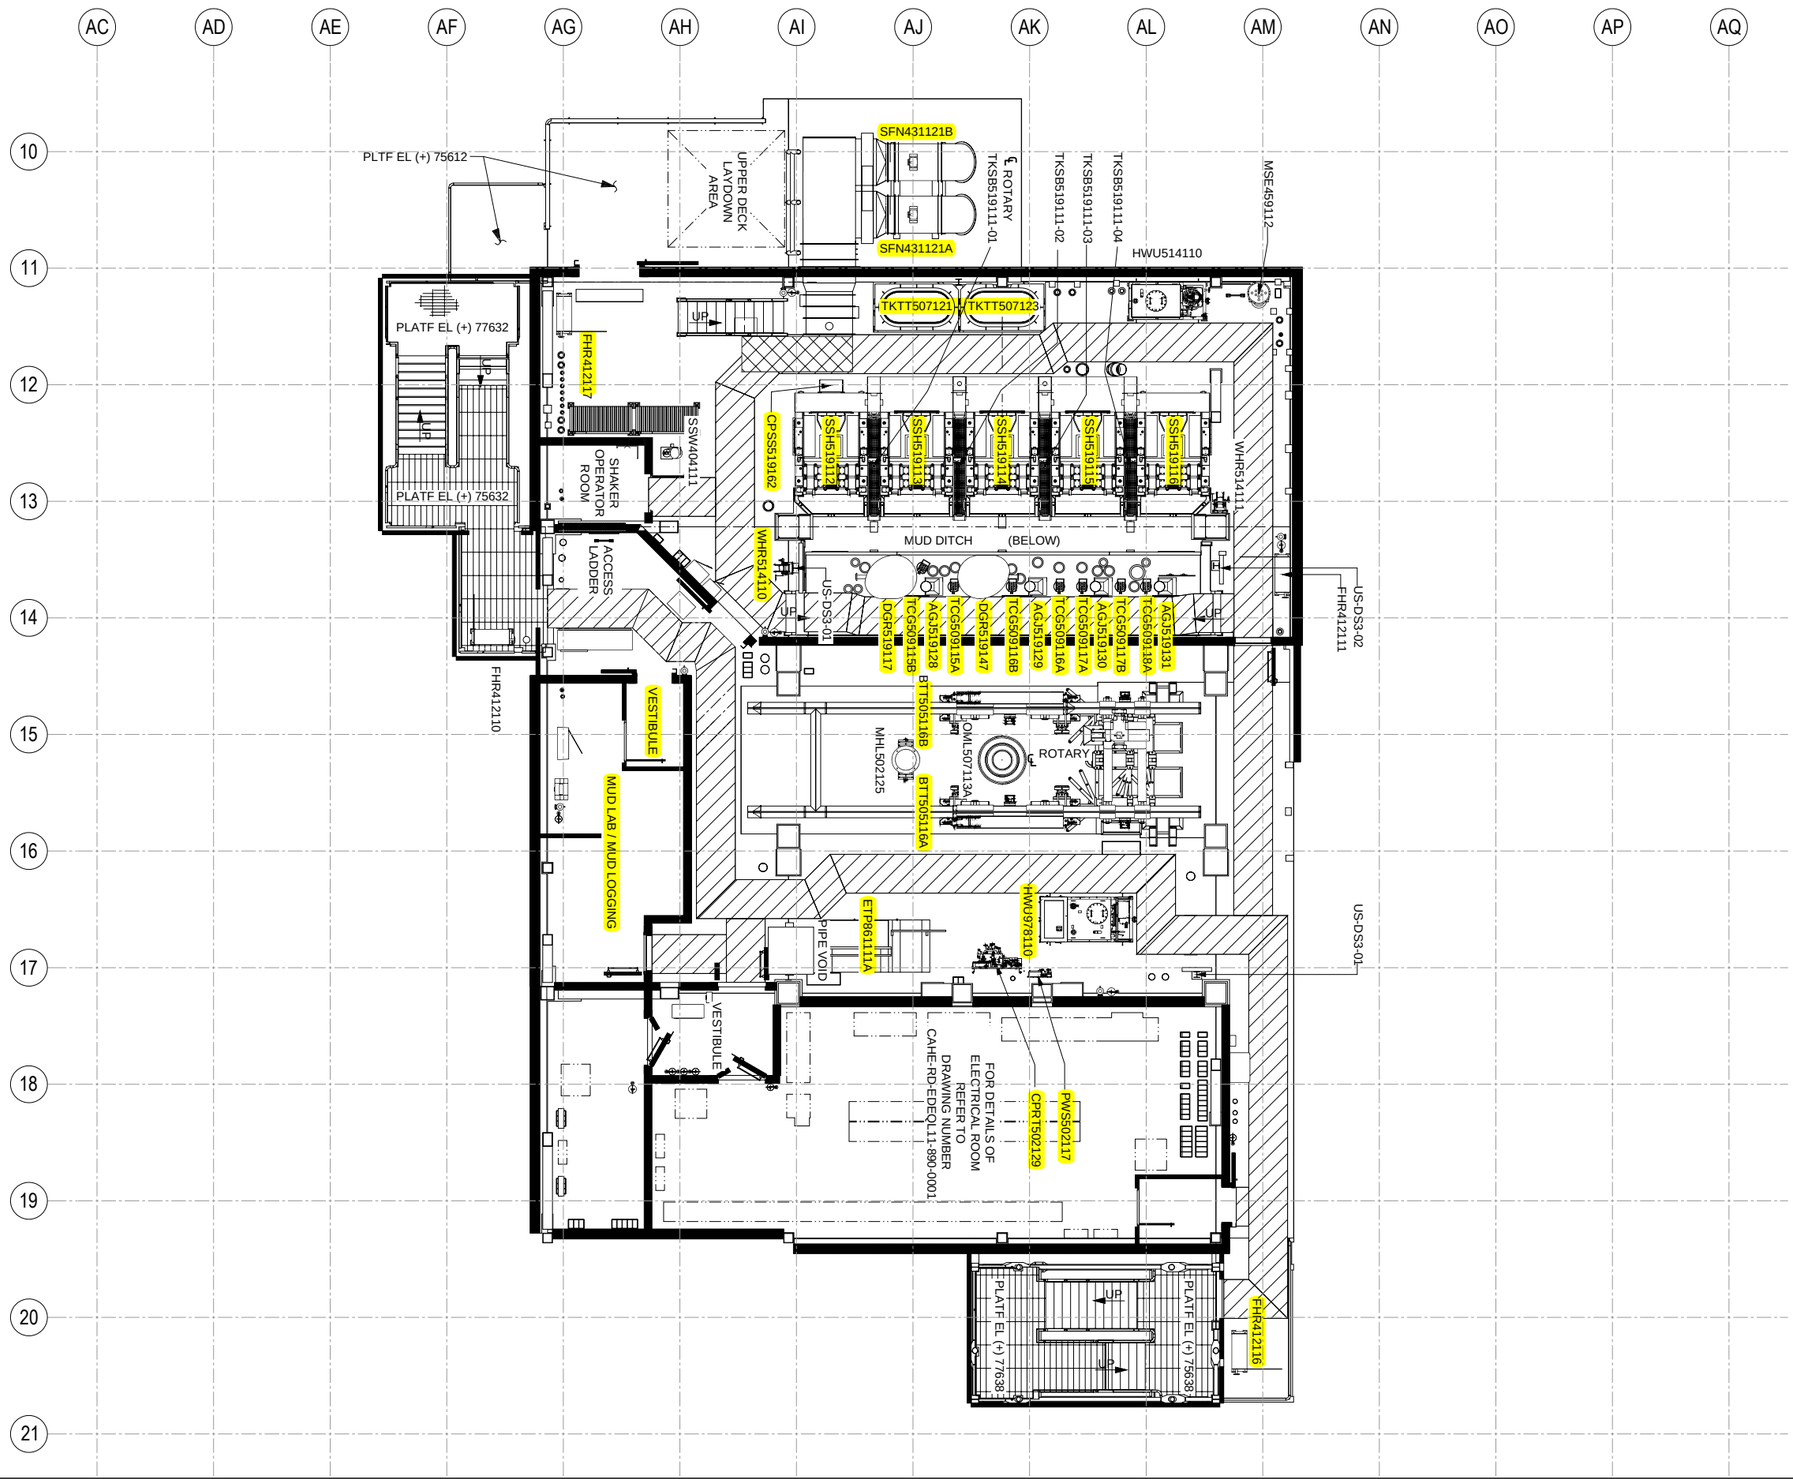

LICENSED PROFESSIONAL ENGINEER
05751
G.L. Scott Humber
28-Jan-2022
DATE
NEWFOUNDLAND & LABRADOR

PROVINCE OF NEWFOUNDLAND AND LABRADOR
pegnl
ENGINEERING PERMIT
N0340
AKER SOLUTIONS CANADA INC.
04850
Signature or Member Number
(Member-in-Responsible Charge)

NO.	DRAWING NUMBER	DRAWING TITLE
1		

REFERENCE DRAWING

REV	DATE DD/MM/YYYY	ORIG.	CHKR.	ENG.	APPR.	DESCRIPTION
		BA	BD	SH	DF	
D0	27/01/2022	BA	BD	SH	DF	ISSUED FOR CONSTRUCTION

AkerSolutions™
SUITE 511,
215 WATER STREET
ST. JOHN'S, NL,
CANADA, A1C 6C9

Hebron

THIS DRAWING MAY NOT BE RELEASED IN WHOLE OR IN PART WITHOUT THE EXPRESS WRITTEN PERMISSION OF EXXONMOBIL CANADA PROPERTIES AS OPERATOR AT HEBRON.

PROJECT: HEBRON OPERATIONS EPCM
MOC No: N/A

TITLE:
DES-UD
DES EQUIPMENT ARRANGEMENT
UPPER DECK
TOS EL. 75600

JOB No:	DRAWING No:	REV.:
A2111	CAHE-ZM-LDEQL-10-000-0004	D0

'No Associated Operations Master'